
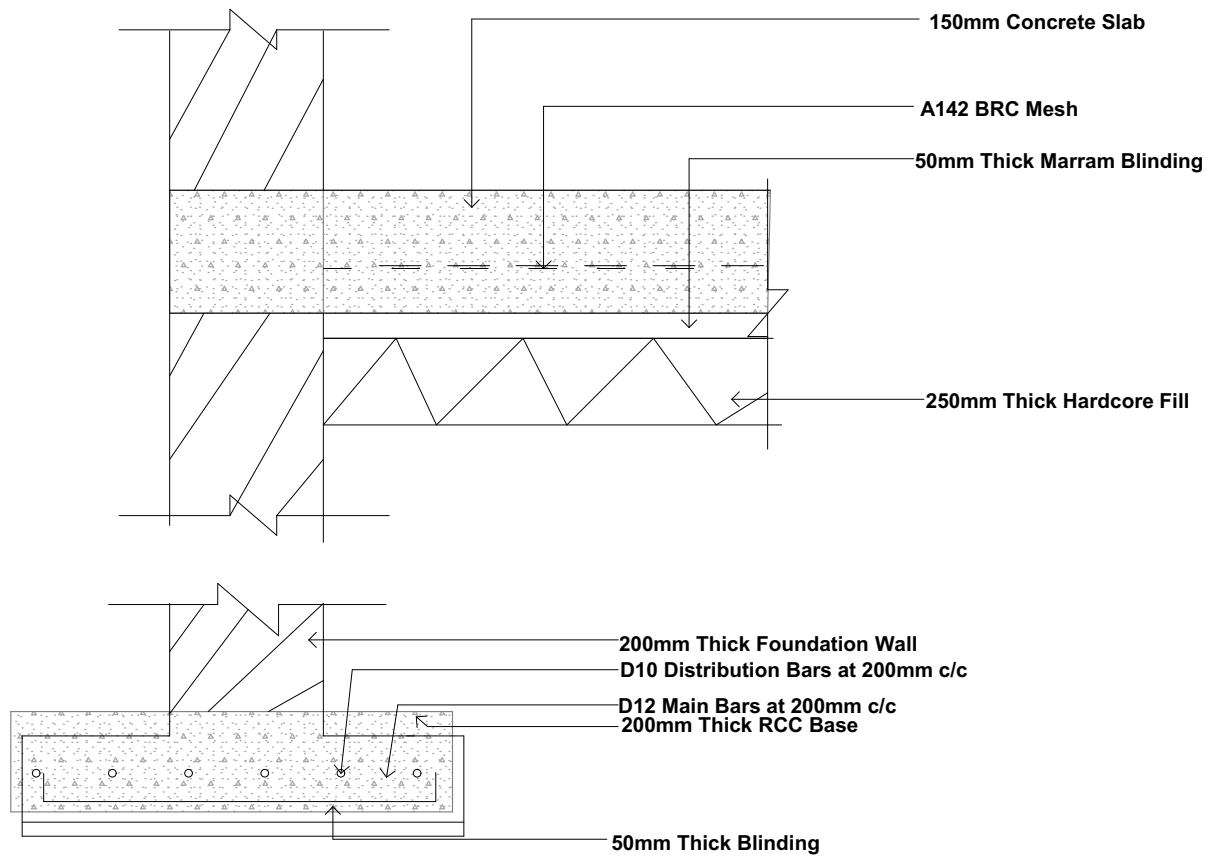
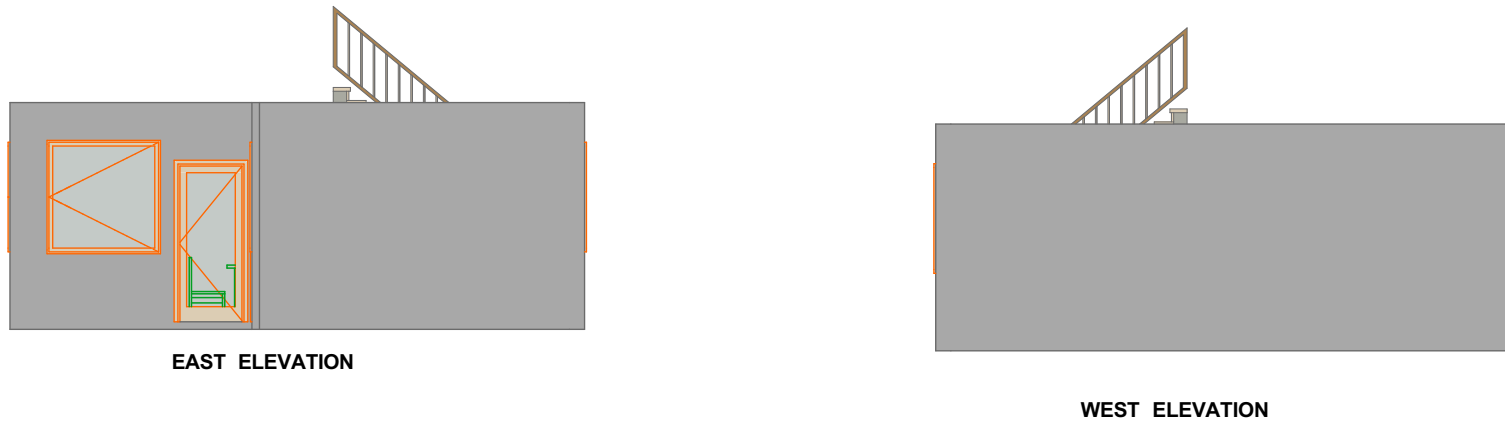
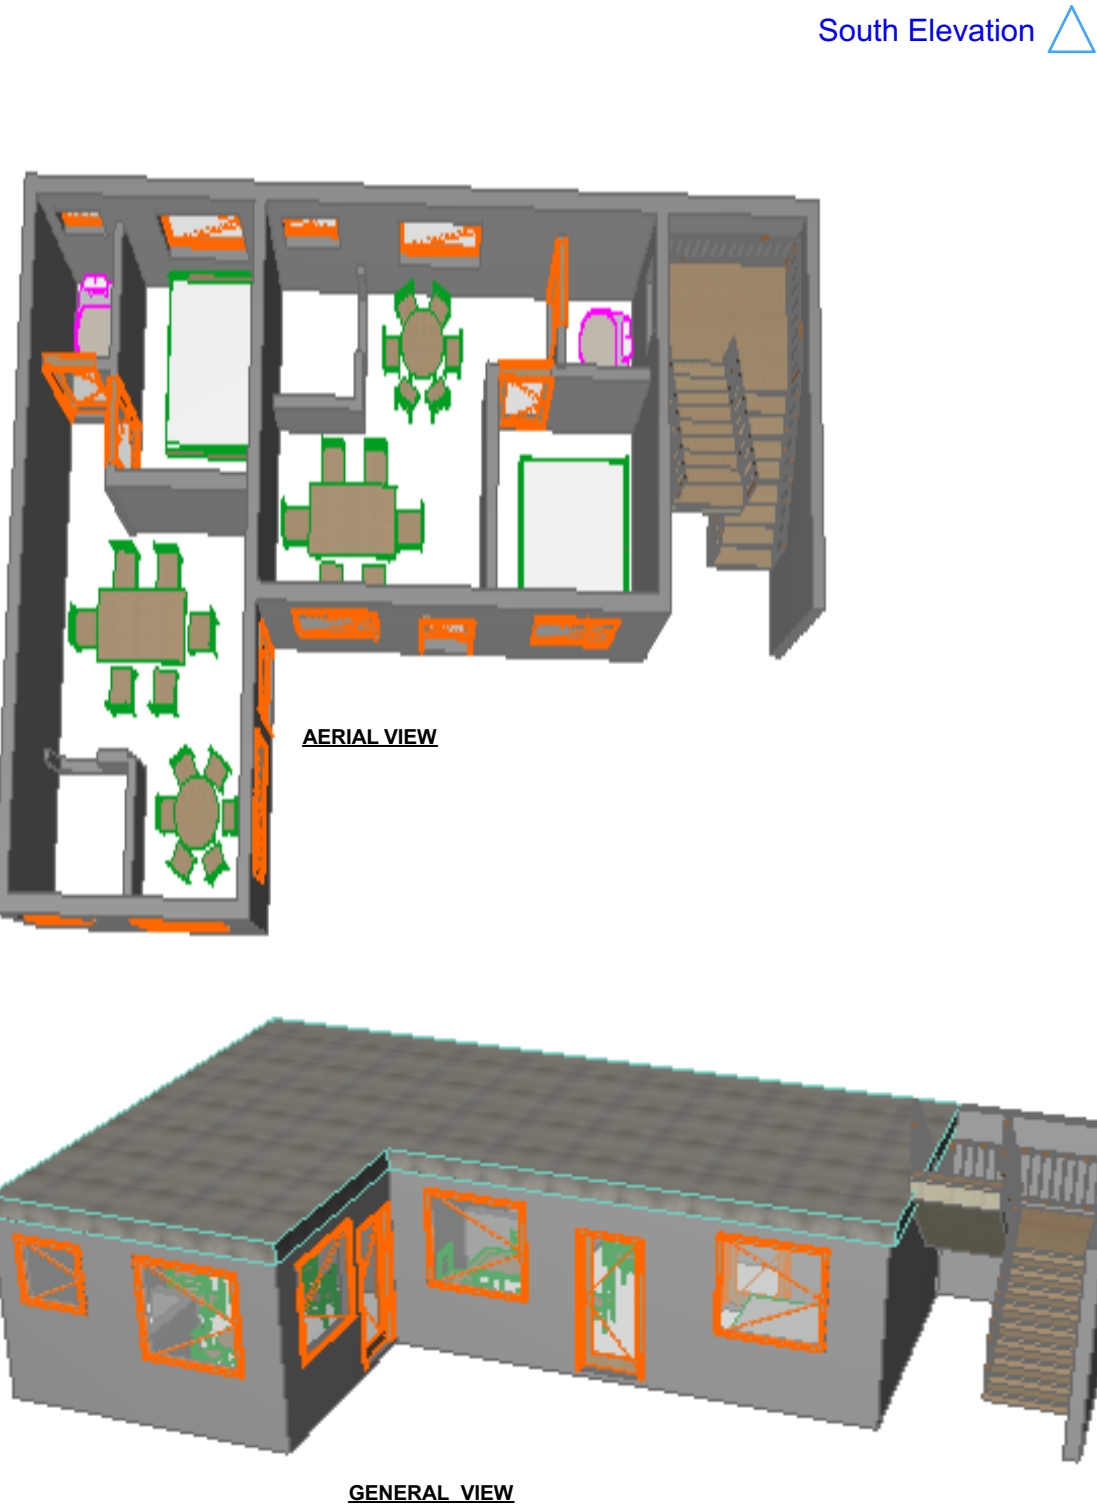
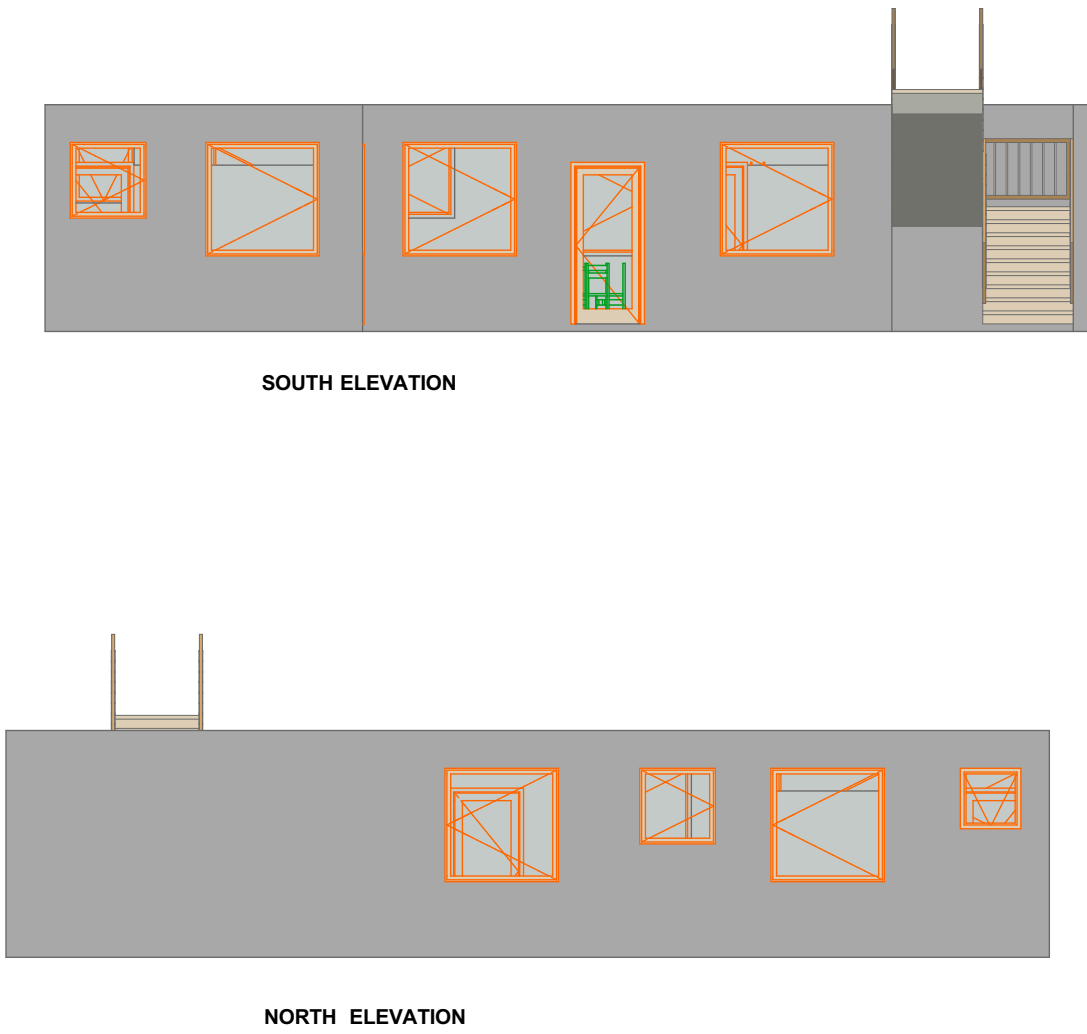


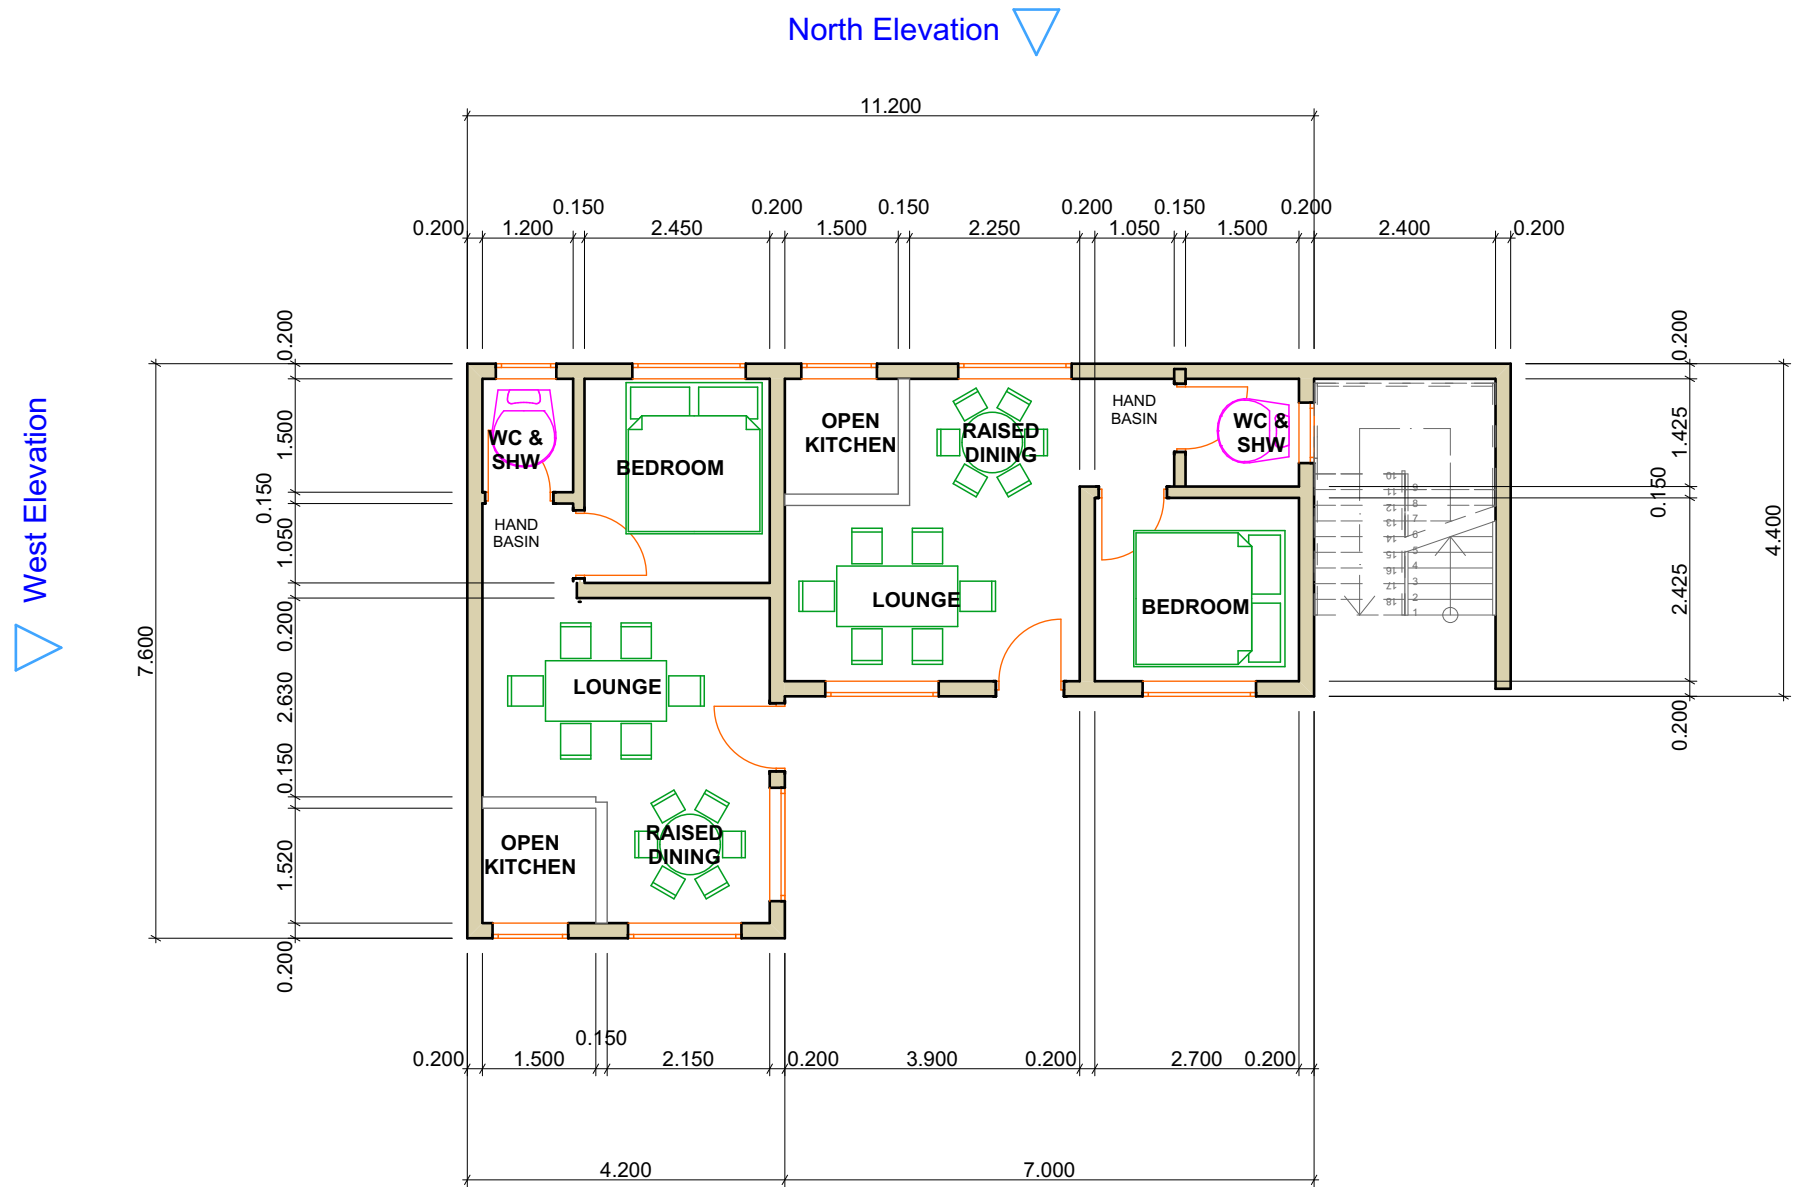

FOUNDATION DETAIL

NOTES

1. ALL WORKS BE CARRIED OUT IN ACCORDANCE WITH THE LOCAL AUTHORITY REGULATIONS
2. ALL FIGURED DIMENSIONS BE TAKEN IN PREFERENCE WITH THE SCALED DIMENSIONS.
3. ALL DIMENSIONS TO BE PROVIDED ON SITE AND SETTING OUT APPROVED BY THE ARCHITECT.
4. DEPTH OF FOUNDATION BE DETERMINED ON SITE.
5. All conduits must be laid before plastering works
6. All superstructure walls be constructed at 2500mm high from the slab.
7. ALL WALLS BE REINFORCED WITH HOOP IRON AT EVERY ALTERNATE COURSE
8. ALL DIMENSIONS ARE IN MILLIMETERS (MM)
9. All slab at grade to be poured on 1000 gauge DPM to a slope of avge 5%
10. Window sills must be finished before internal finishes.

ARCHITECT.

DICKENS LIYAYI

CLIENT

ANNE BRITISH

PROJECT

PRPOSED RENTAL HOUSES

DRAWING TITLE	FLOOR PLAN AND ELEVATIONS.
Modified by	Date
DICKENS LIYAYI	
Checked by	Date
AGGREY M.M.	
Drawing Scale	1:100