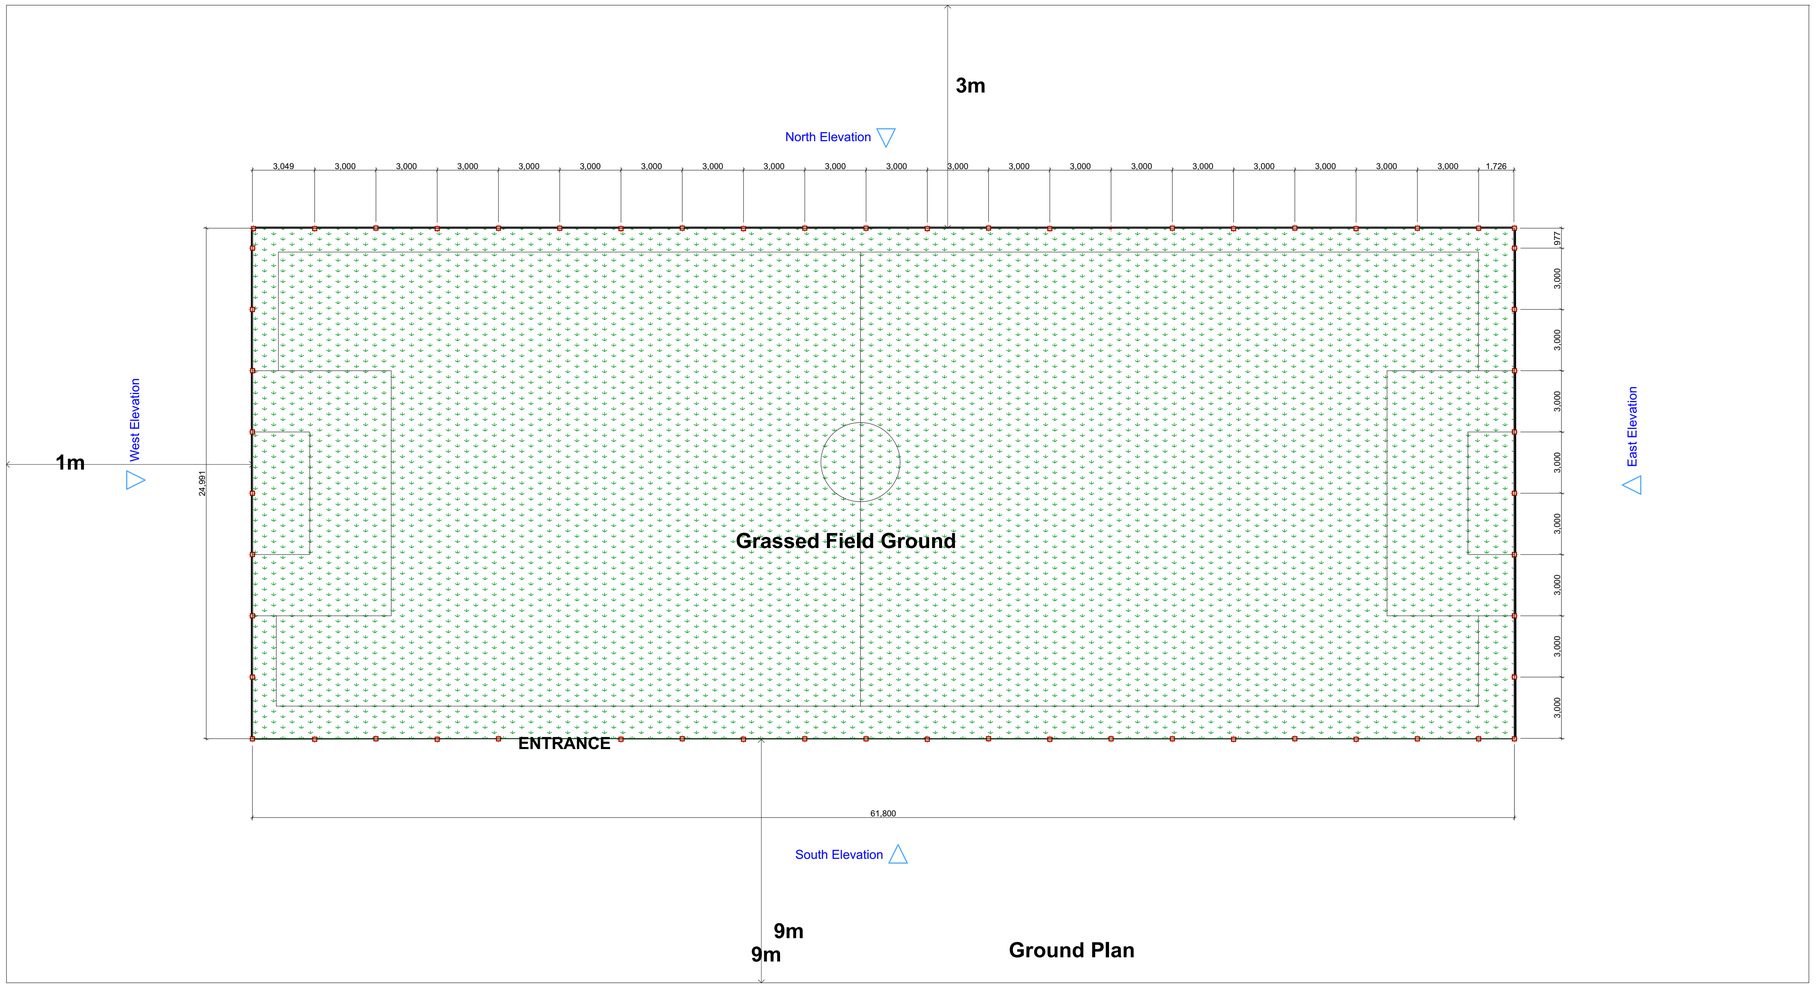

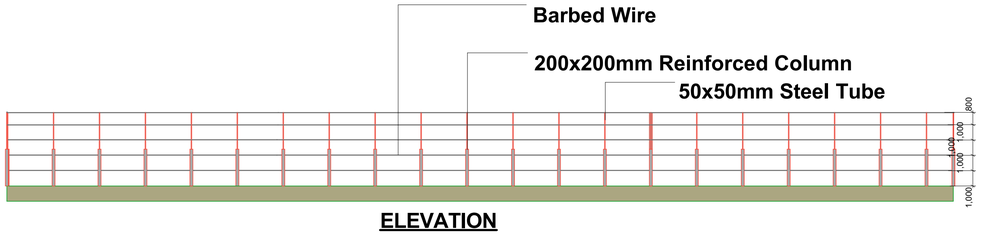

ELEVATION

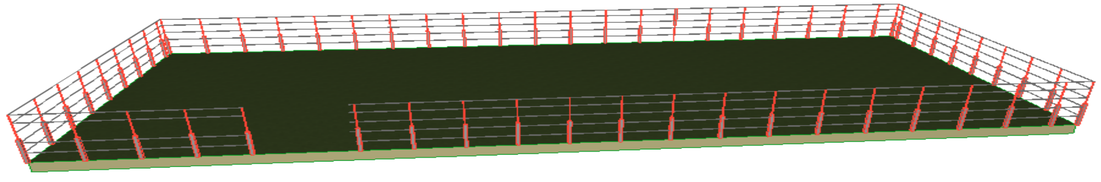

GENERAL VIEW

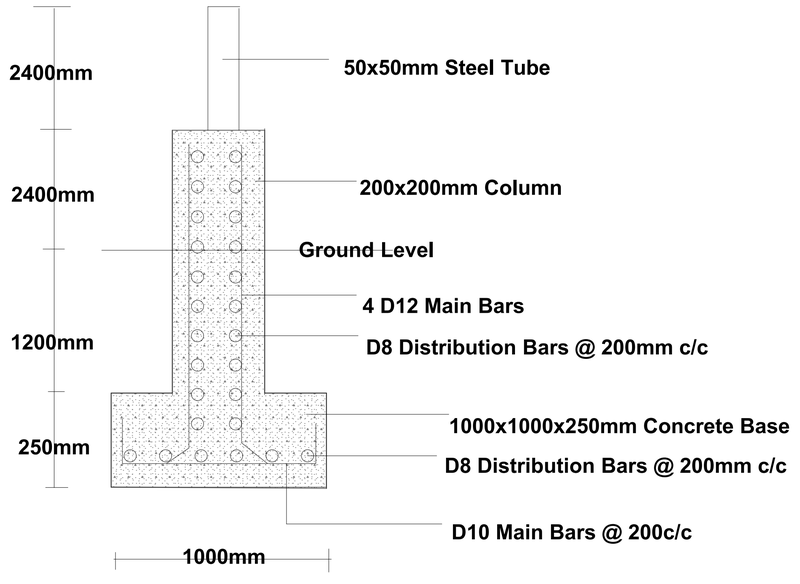

Column Detail

NOTES.

1. The total number of columns is 59
2. The depth of the column is 1m deep.
3. Column base of all all column ia 1000x1000x250mm
4. All measurements are in mm unless otherwise sateted.
5. Bothe the chain link and barbed wire to be approved by the client or contractor.
6. The grass has already been planted hence should not be quated for.
7. All reinforcements be done as per the drawing unless otherwise stated.
8. The height of the excuvation shall be determined on site

RevID	ChID	Change Name	Date
		Revision History	

ARCHITECT

TSL Thrifty Solutions Limited

CLIENT

CHILDREN HOME

FIELD PLAN

SCALE

1:150