

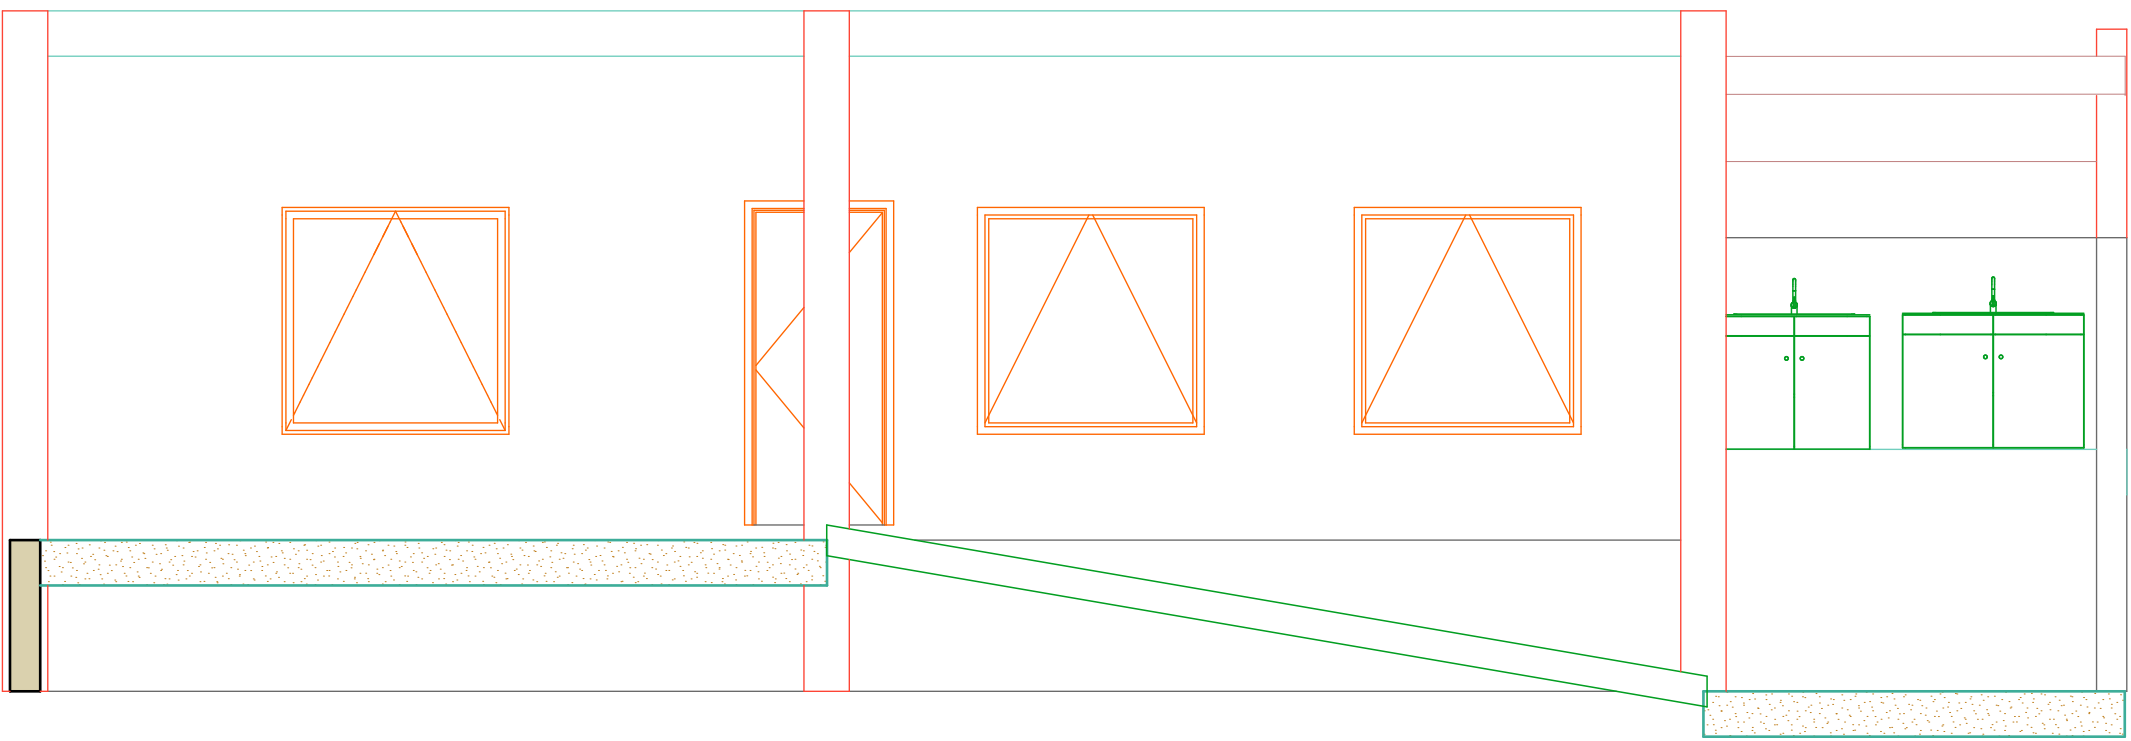



FLOOR PLAN

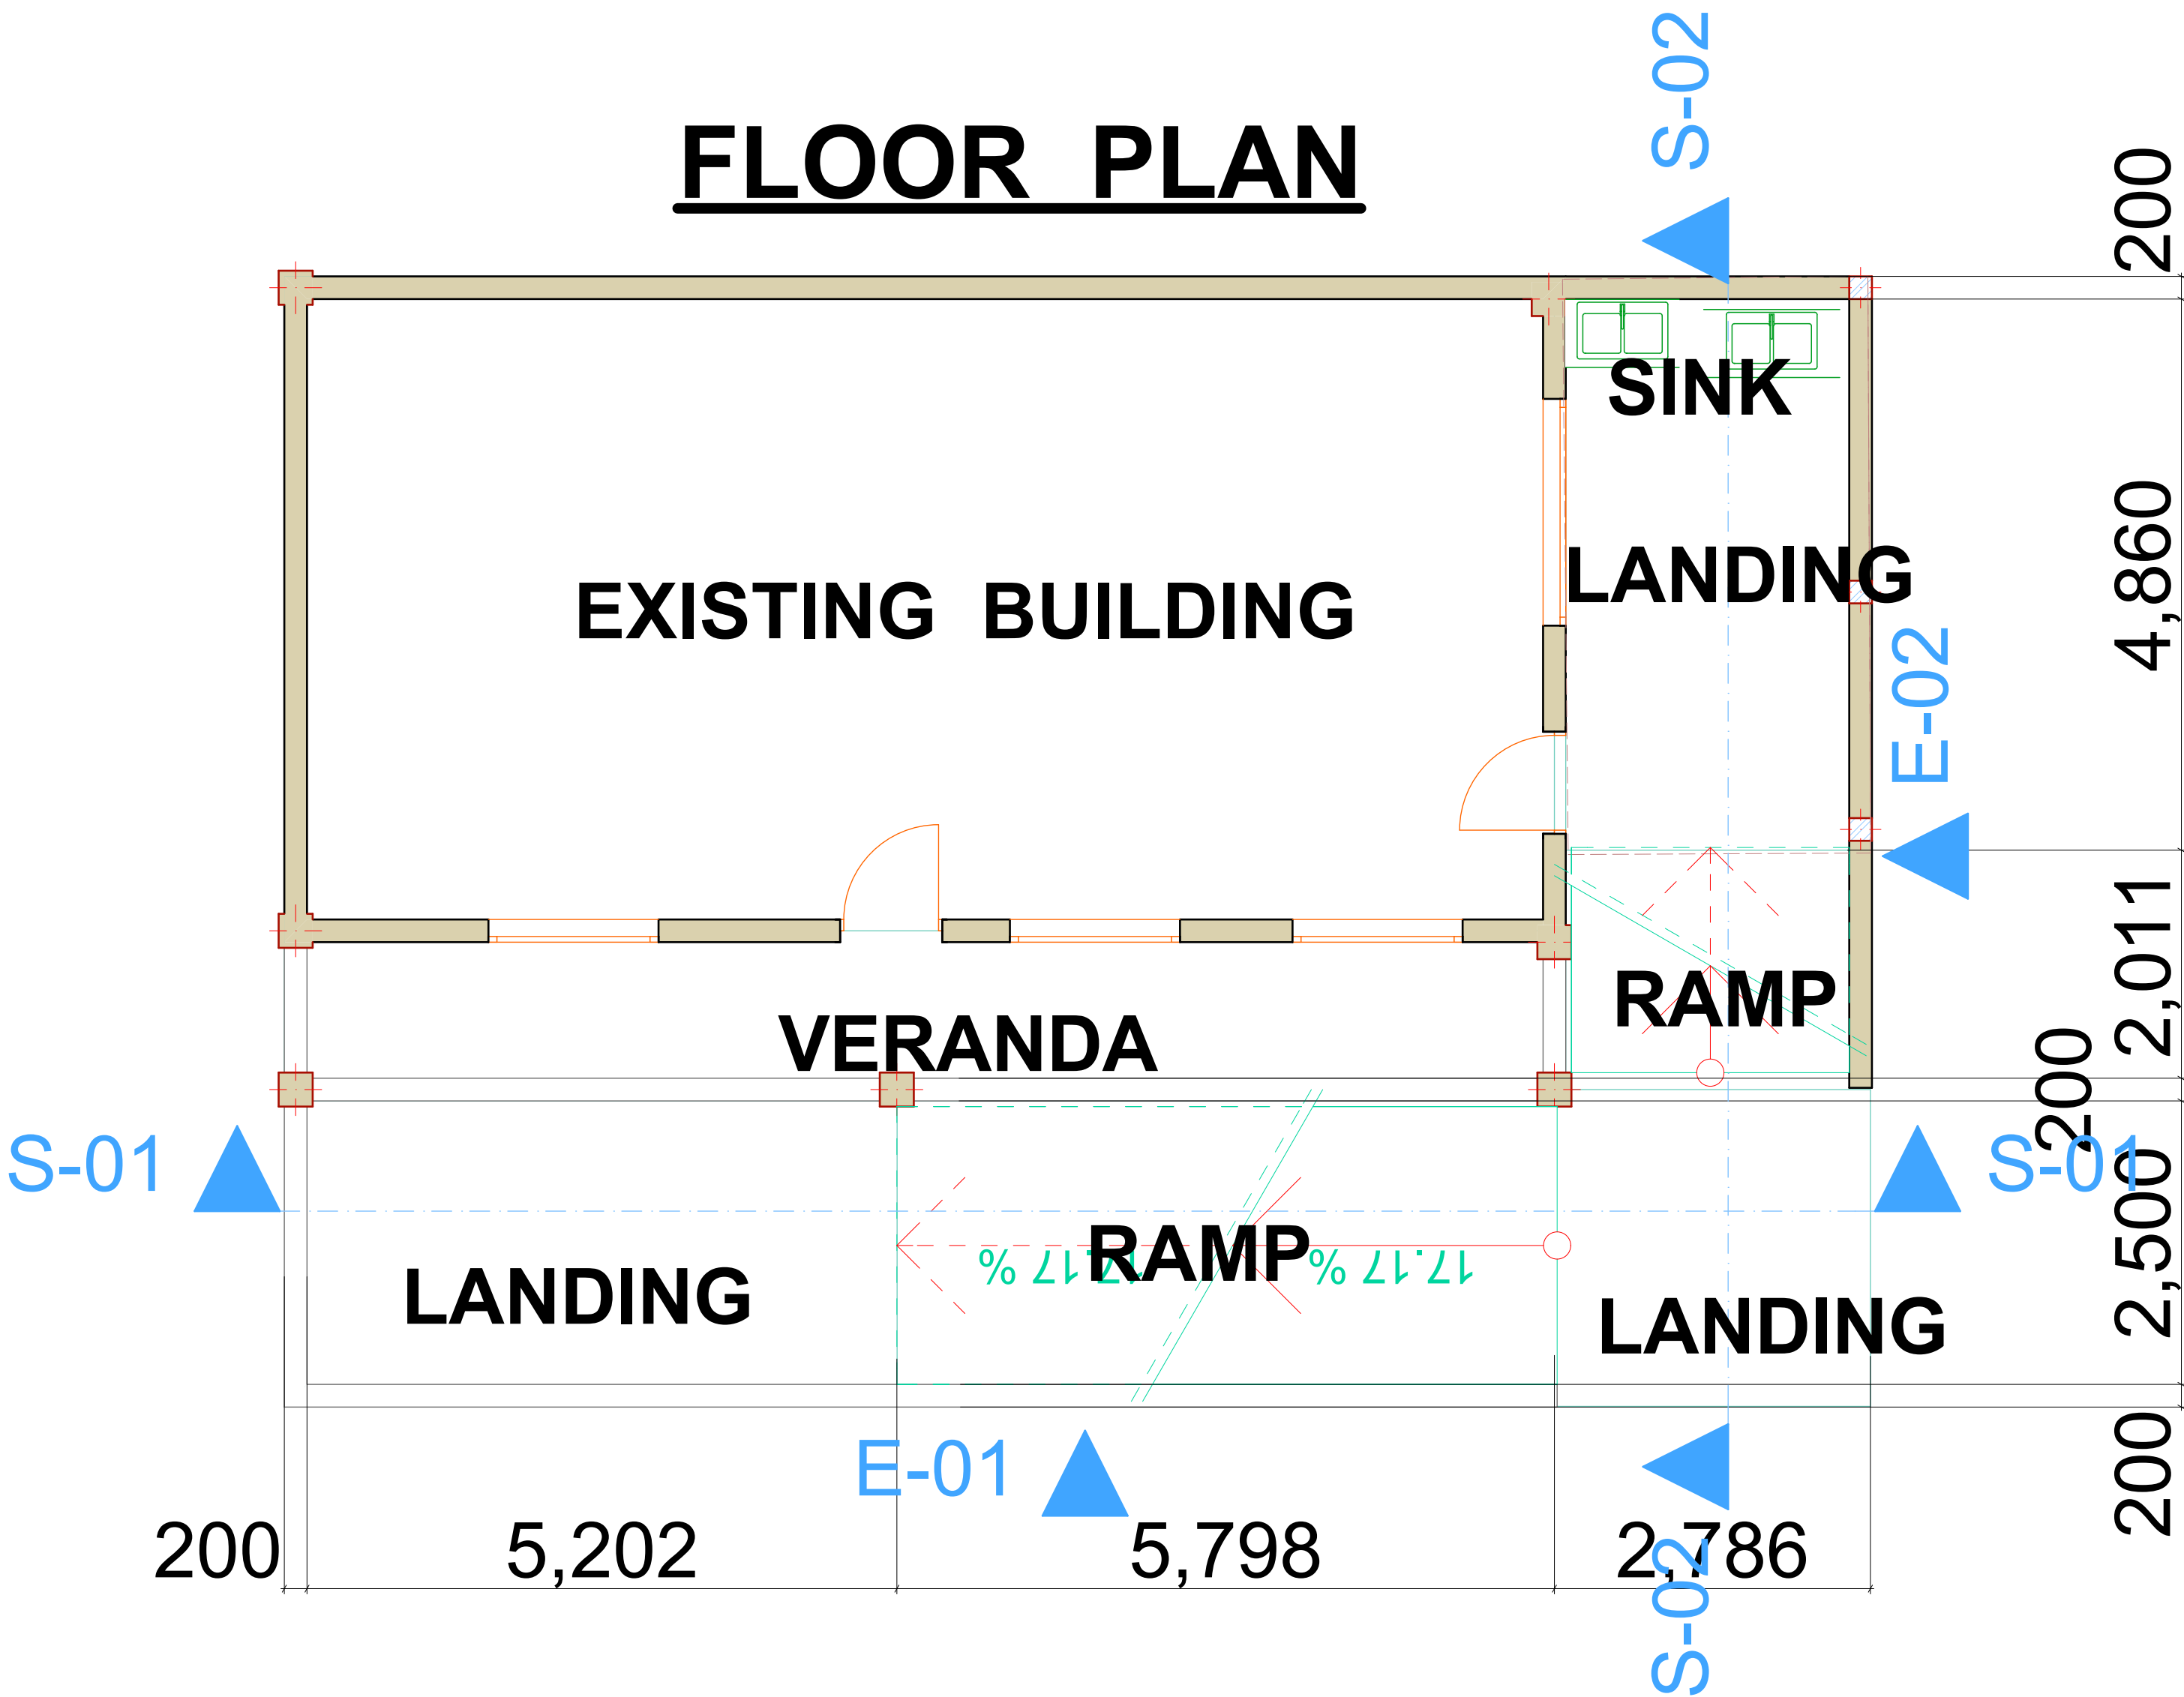


SECTION 02

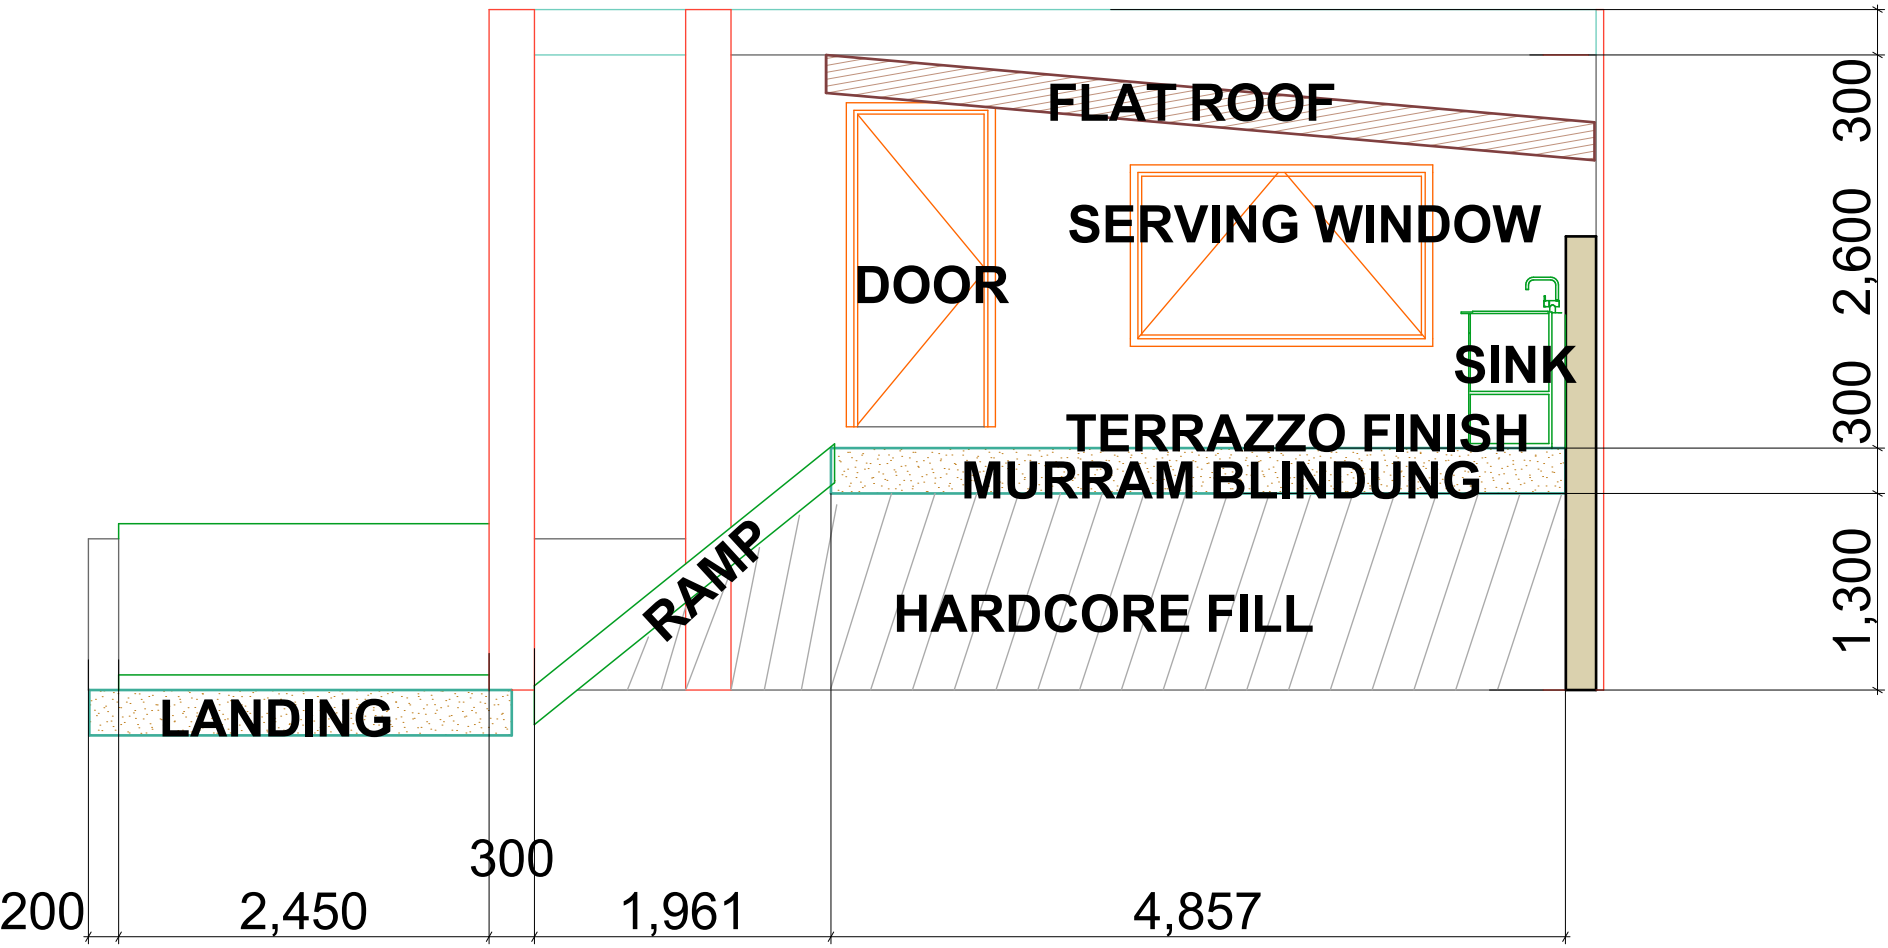


SECTION 02

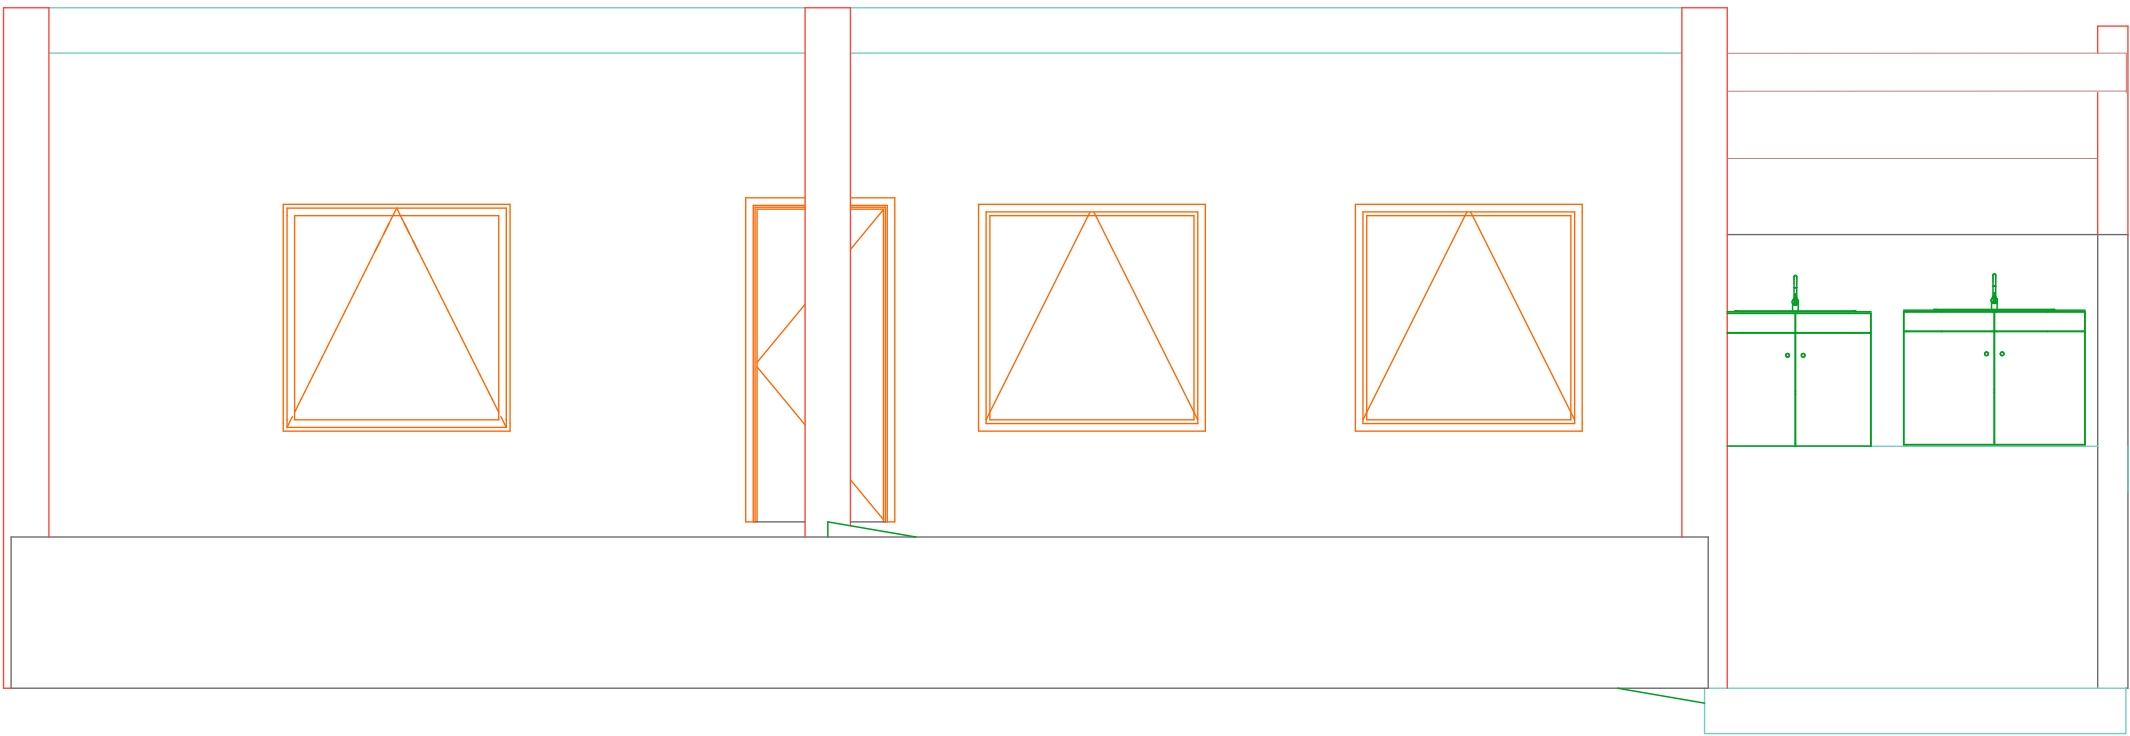

ELEVATION 01

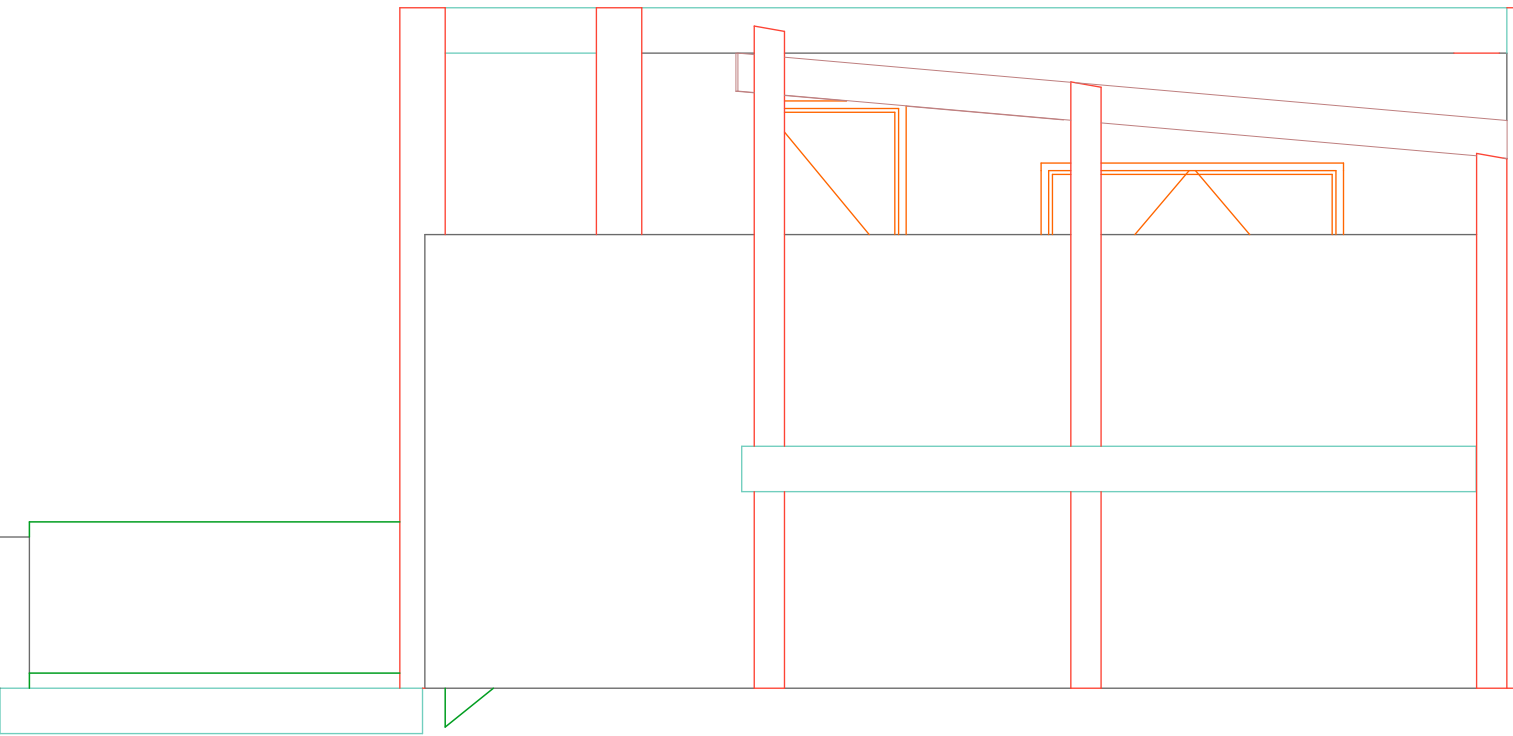

ELEVATION 02

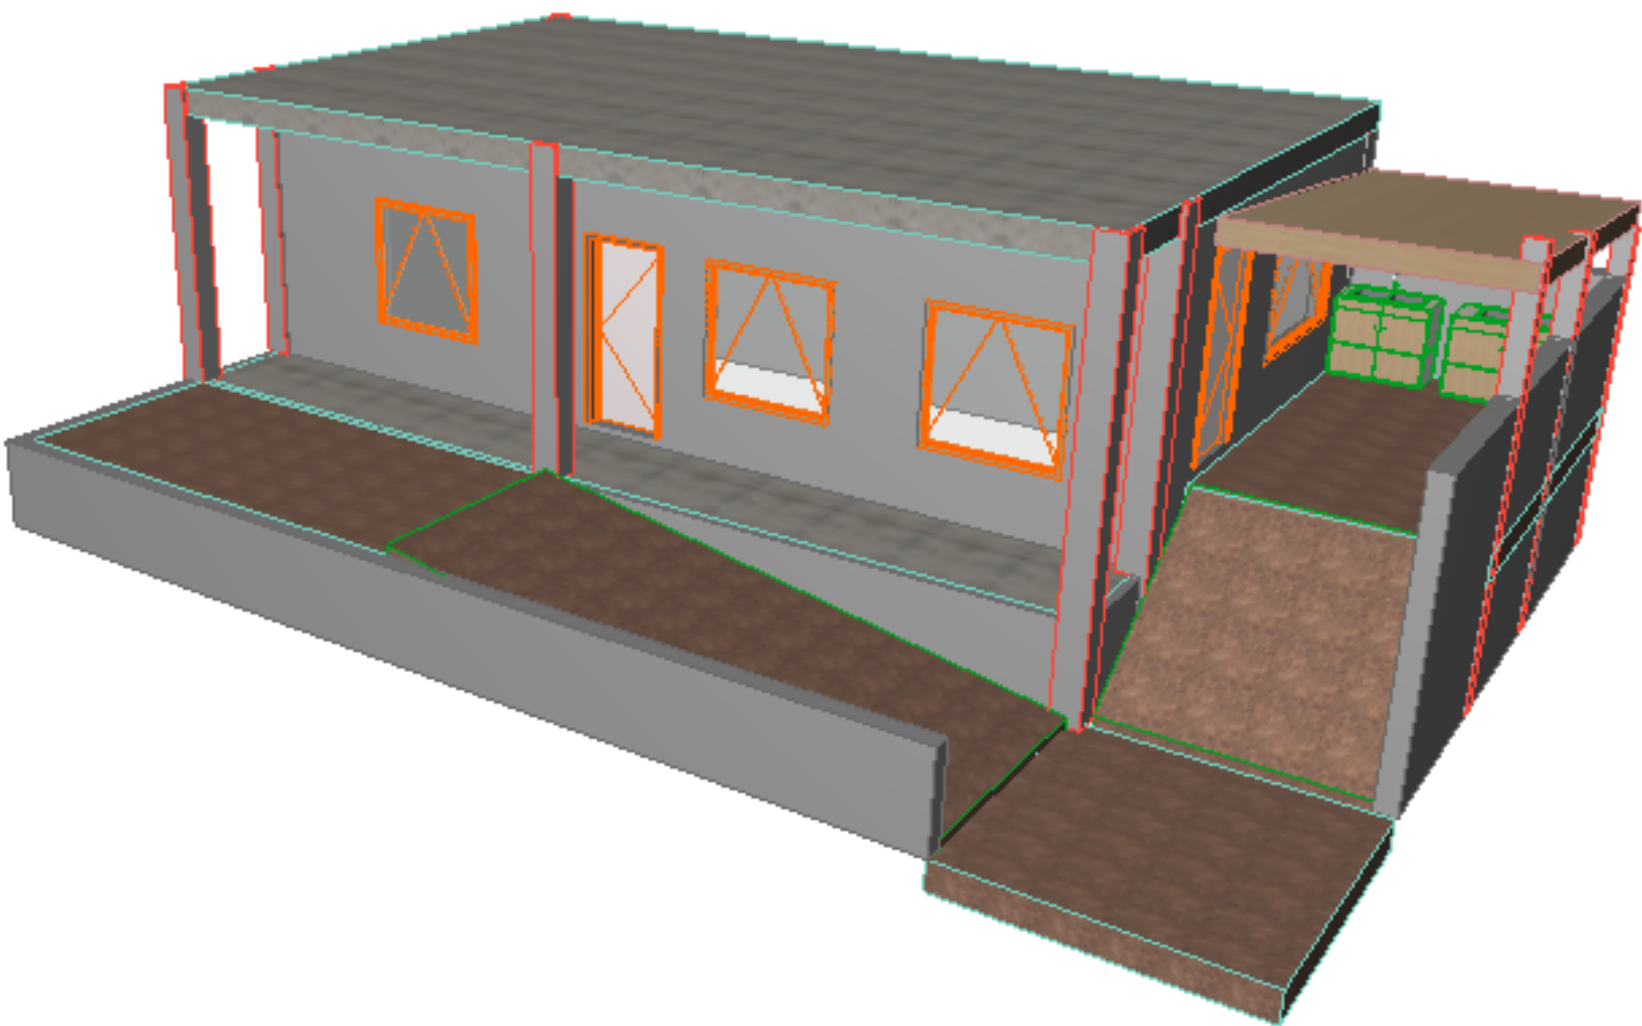

GENERAL VIEW

NOTES

1. All measurements are in millimeters.
2. All dimensions to be adjusted as per the site condition in consultation with the arch or contractor
3. All works be done as per the local authorities and building code requirements.
4. Hardcore fill should be well laid in layers and compacted in small units uniformly.
5. Murrum blinding should be atleast 20mm thick well compacted into two equal layers.
6. Coocrete waist should be atleast 100mm thick reinforced with A142 BRC mesh
7. The heigt of the sink from landing is approximately 1m high with running water taps.
8. the parapet wall should be 1200mm high from the top landing.
9. The flat roof is supported with a 200x200mm square tube steel

REVISION NOTES

DATE	DESCRIPTION	SIGN

ARCHITECT.

DICKENS LIYAYI

CLIENT

CHILDREN HOME BOARD OF
MANAGEMENT (NAIROBI)

PROJECT

PROPOSED RENOVATIONS AND
MAINTANANCE ON THE KITCHEN

DRAWING
TITLE

RAMP FLOOR PLAN
ELEVATIONS AND
SECTIONS.

CORNFIMED BY.....

DATE.....

SCALE:
1:50